





Project			Sheet No. of Sheets	
S.R.	Made By	Check by	Date	Supv

LBAM MODELS

SINGLE SPAN PRESTRESSED GIRDER

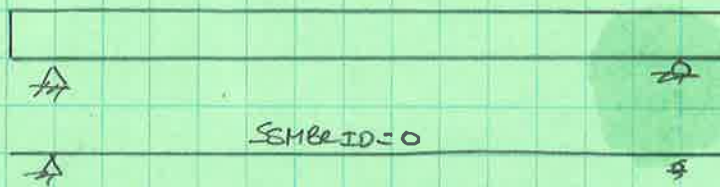

MULTI-SPAN PRESTRESSED GIRDER - SIMPLE SPANS

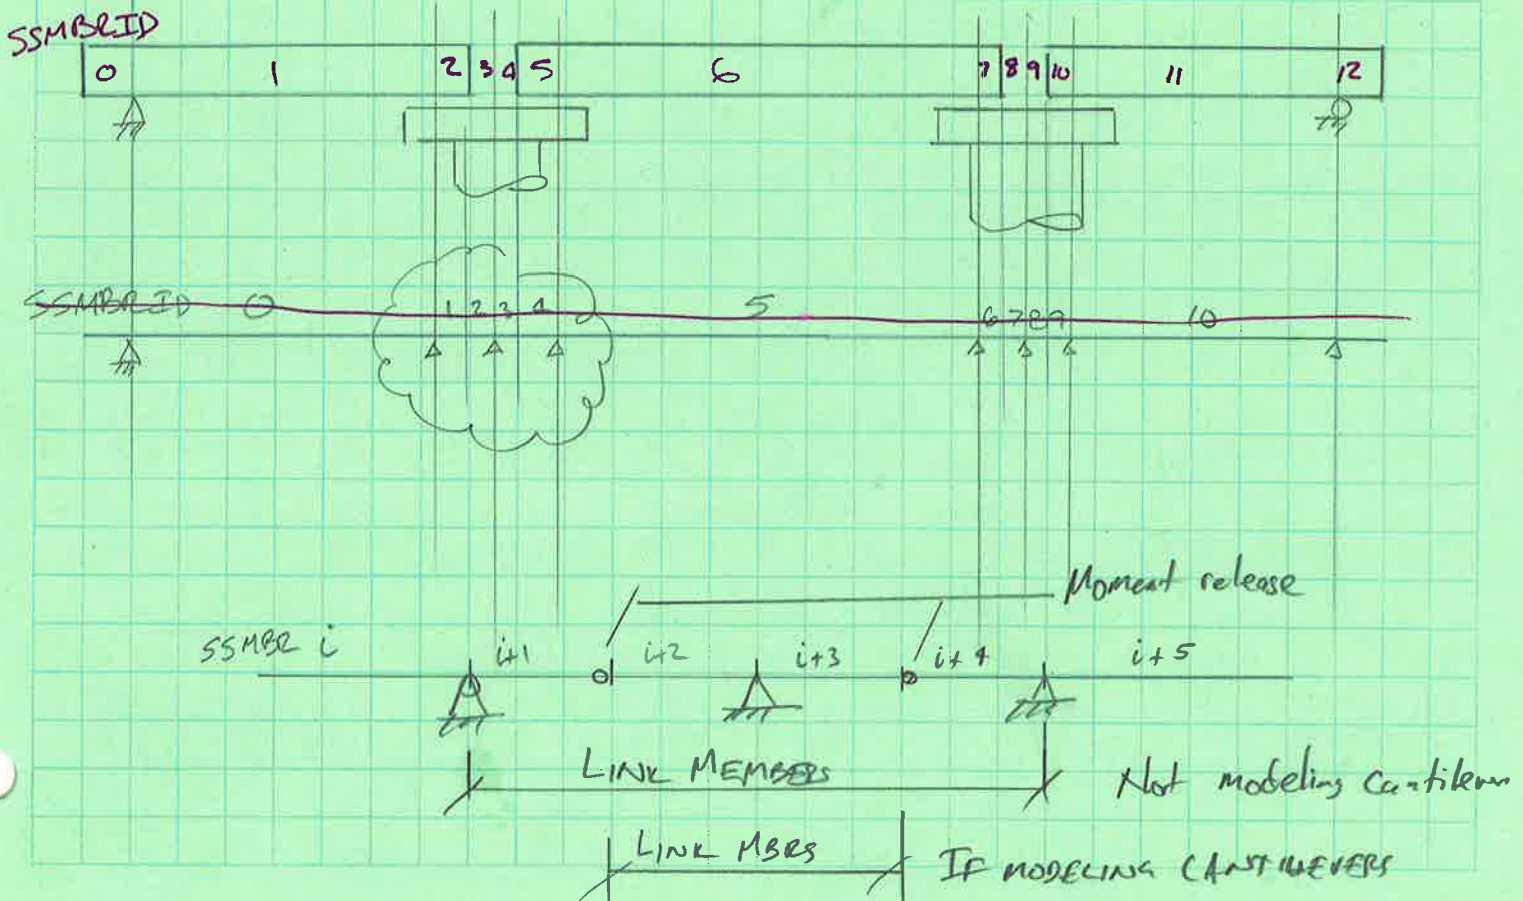





Project			Sheet No. _____ of _____ Sheets	
S.R.	Made By	Check by	Date	Supv

LBAM EXAMPLES

SINGLE SPAN PRESTRESSED GIRDER



MULTIPLE SPAN - SIMPLE SPAN PRESTRESSED GIRDER

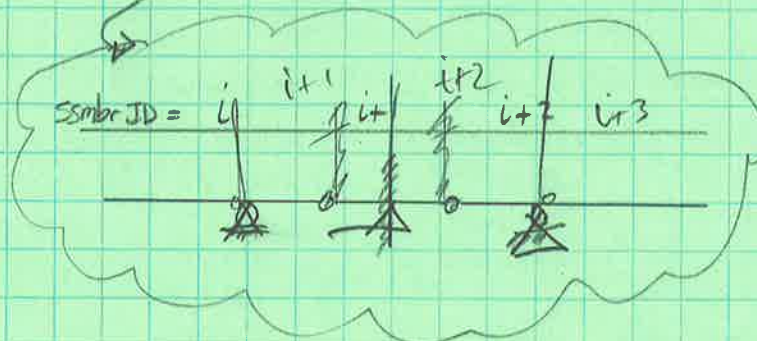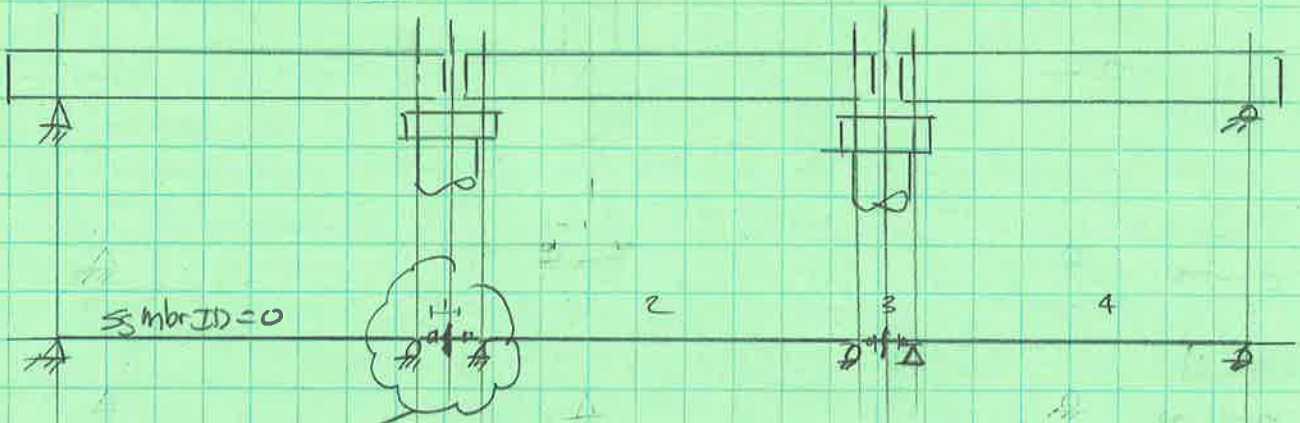




Project		Sheet No. of Sheet	
S.R.	Made By	Check by	Date
		Supv	

LBAM SPAN CONFIGURATION




$$L = \ell_{Pier} - \ell_{Pier} \text{ measured along } \ell_{Girder}$$

TEMPORARY SUPPORT LOCATIONS

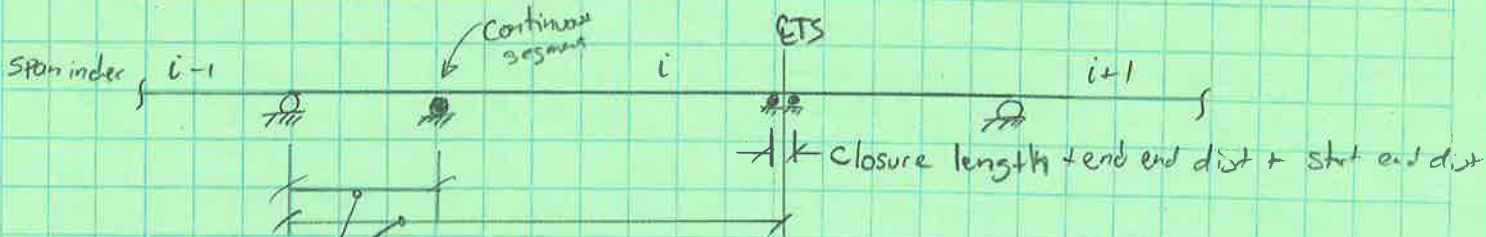

Distance from ℓ_{Pier} measured along ℓ_{Girder}

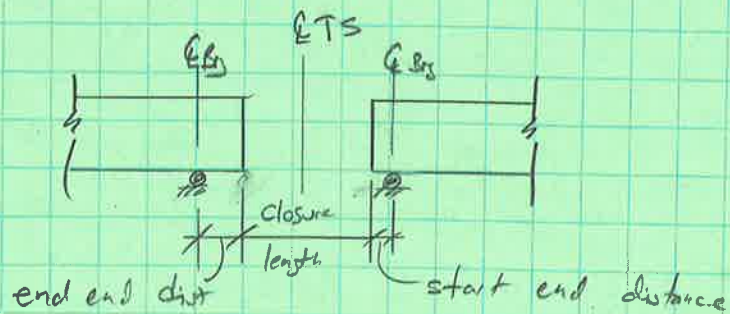





Project		Sheet No. of Sheets	
S.R.	Made By	Check by	Date
		Supv	

LBAM SUPERSTRUCTURE MEMBERS

- One physical girder segment = One LBAM superstructure mbr

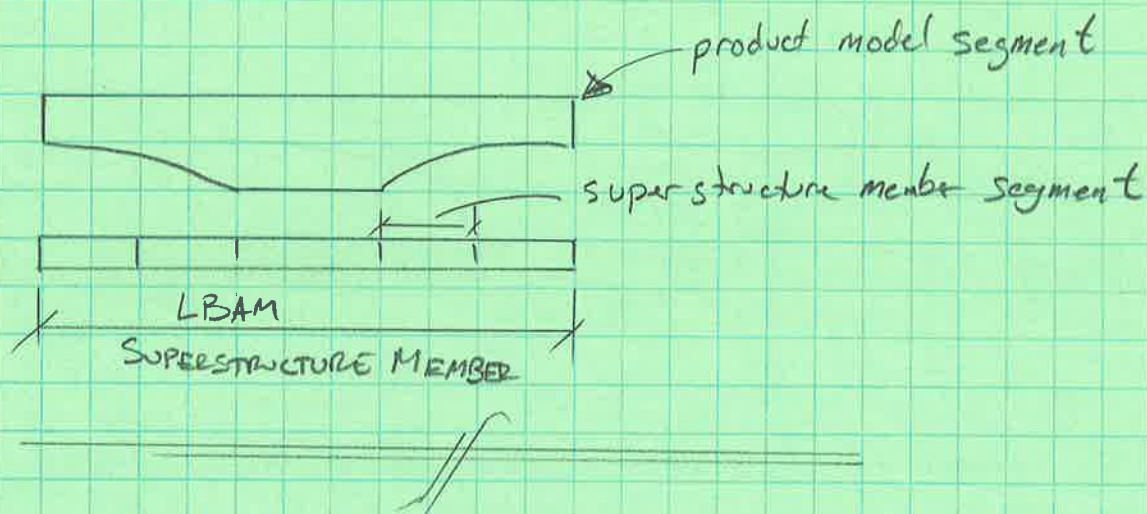


FIRST PRODUCT SEGMENT IN BRIDGE

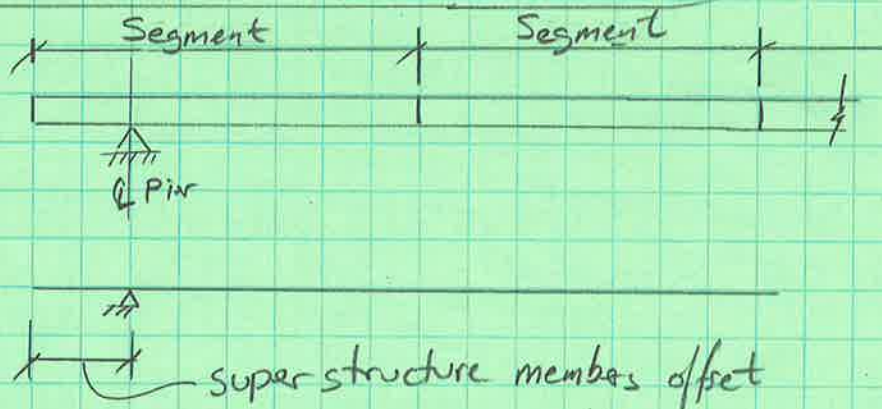




Project				Sheet No.	of	Sheets
S.R.	Made By	Check by	Date	Supv		

SUBSEQUENT PRODUCT SEGMENTS

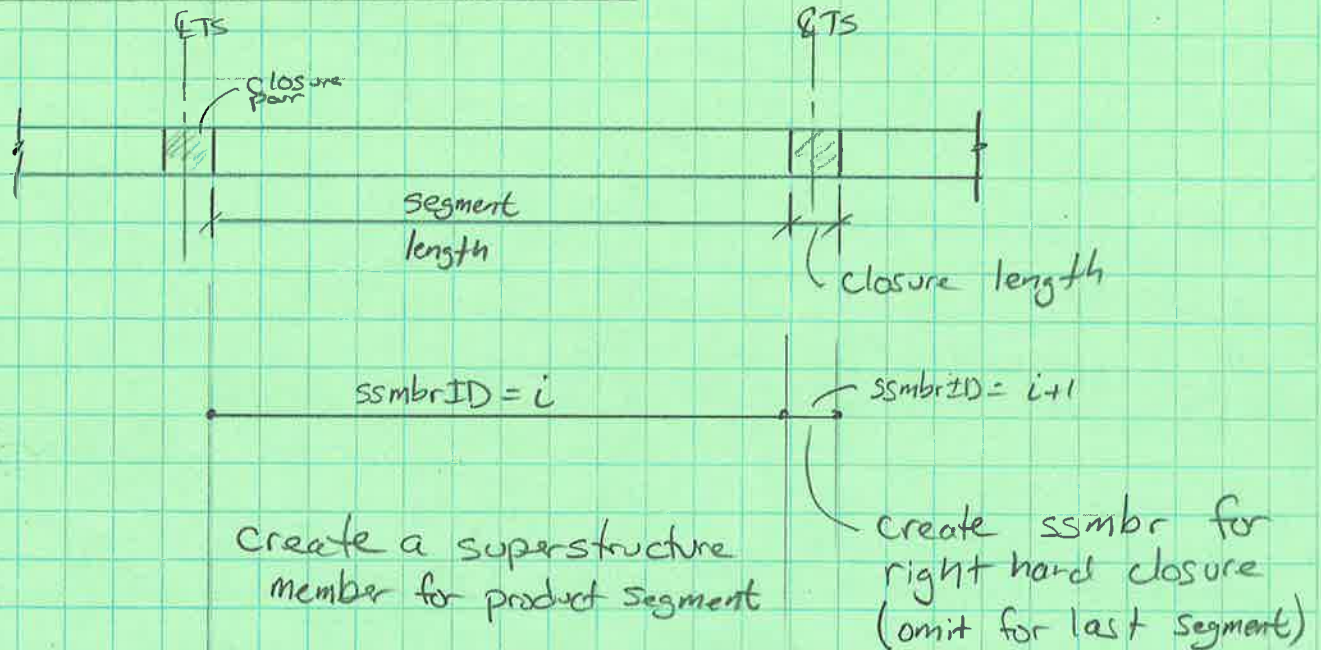

LAST SEGMENT IN GIRDER EXCEPT FOR LAST GROUP

- 2 groups meet at this pier
- end of left girder, start of right girder

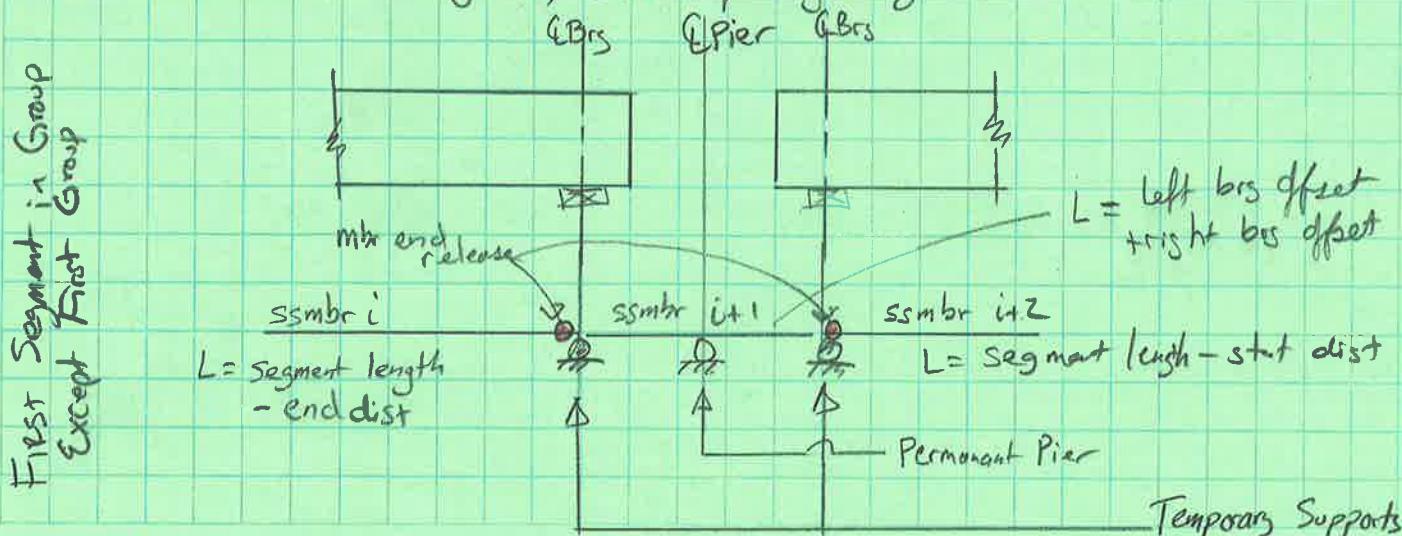


mbr end releases & temp supports removed @ continuity stage



Project		Sheet No. of	
S.R.	Made By	Check by	Date
		Supv	


MULTI-SPAN SIMPLE MADE CONTINUOUS

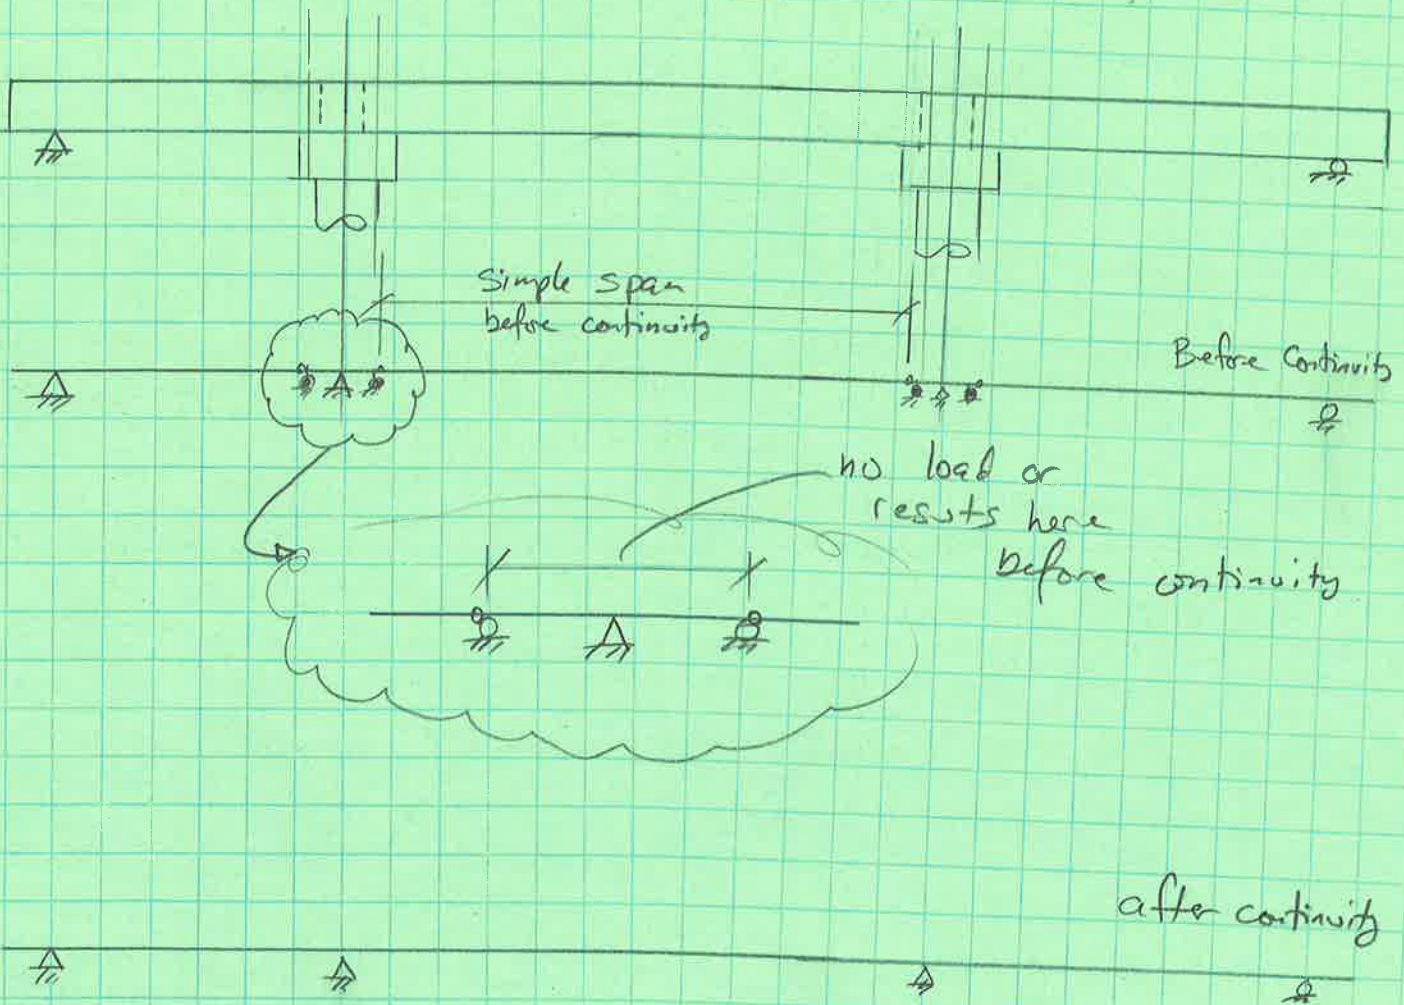



Project		Sheet No.		of	Sheets
S.R.	Made By	Check by	Date	Supv	

SIMPLE MADE CONTINUOUS

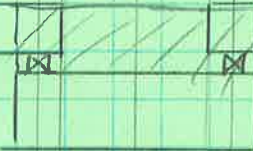

SIMPLE SPAN ANALYSIS
AFTER CONTINUITY

Seg 1



SIMPLE SPAN
BEFORE CONTINUITY



CONTINUOUS BEFORE CONTINUITY




CONTINUOUS AFTER CONTINUITY

NEED PDI
@ & PIER




Project			Sheet No. _____ of _____ Sheets	
S.R. _____	Made By _____	Check by _____	Date _____	Supv _____

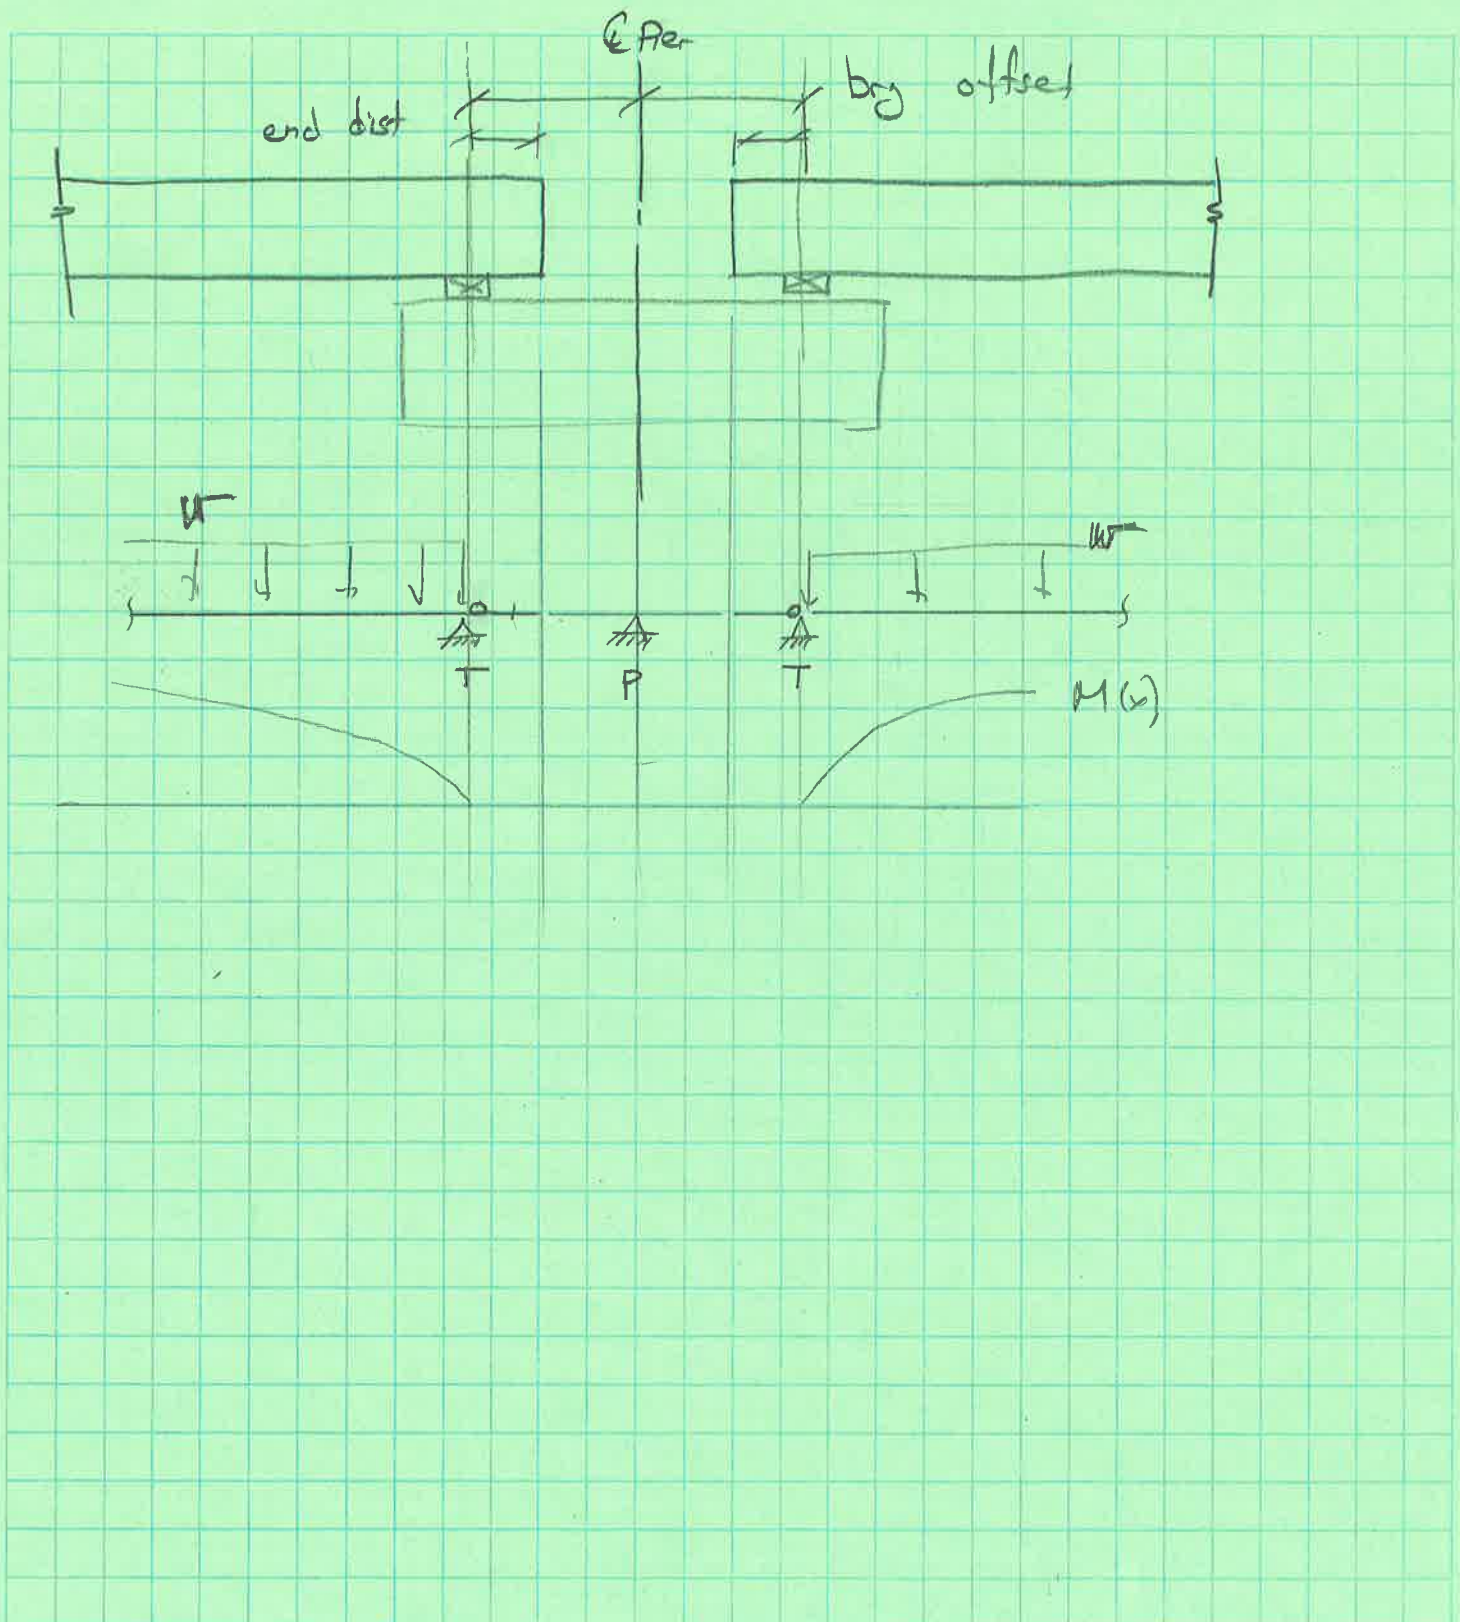




Project			Sheet No. _____ of _____ Sheets	
S.R.	Made By	Check by	Date	Supv

BRIDGE DEFINITION

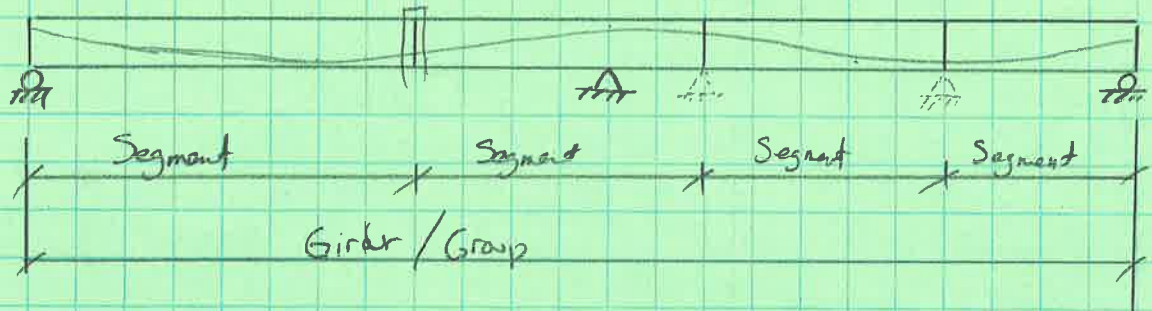

LBAM

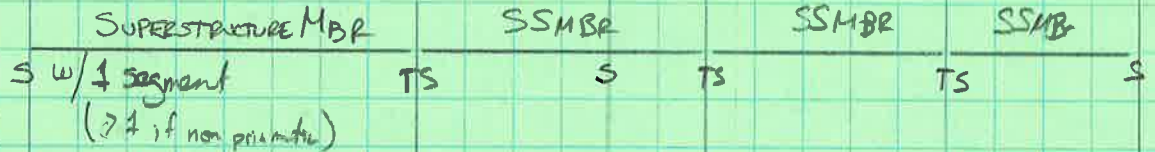

FEM2D




IF LBAM HAS MULTI-SEGMENT SUPERSTRUCTURE MEMBERS
FEM2D HAS NODES/MEMBERS FOR EACH SEGMENT



Project			Sheet No.	of	Sheets
S.R.	Made By	Check by	Date	Supv	

LBAM

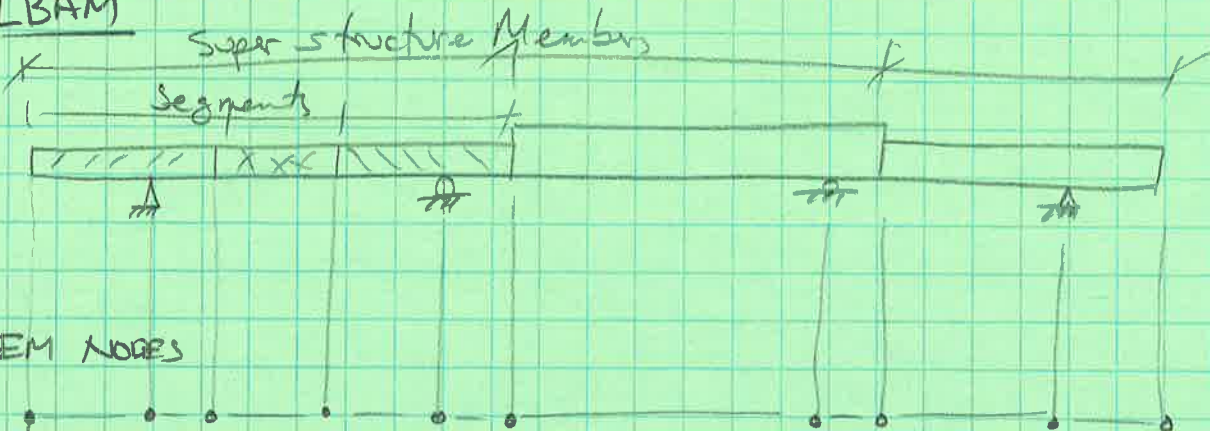


BRIDGE

GIRDER SEGMENTS

LBAM


LBAM SUPER STRUCTURE MEMBERS

FEM NOES

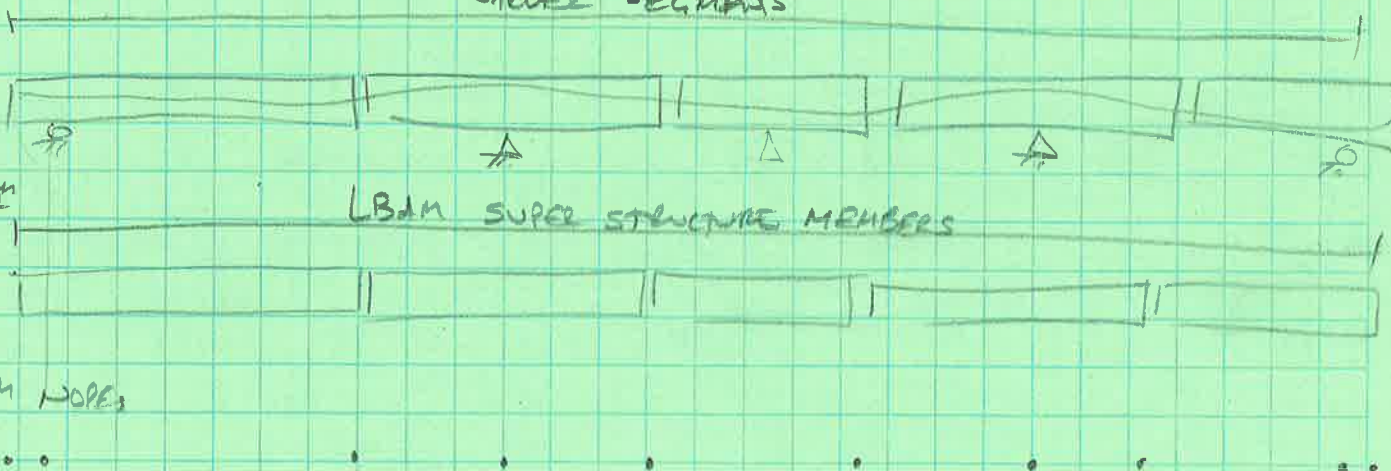




Project LBAM @ ERECTION TOWER		Sheet No. _____ of _____ Sheets	
S.R.	Made By	Check by	Date
			Supv

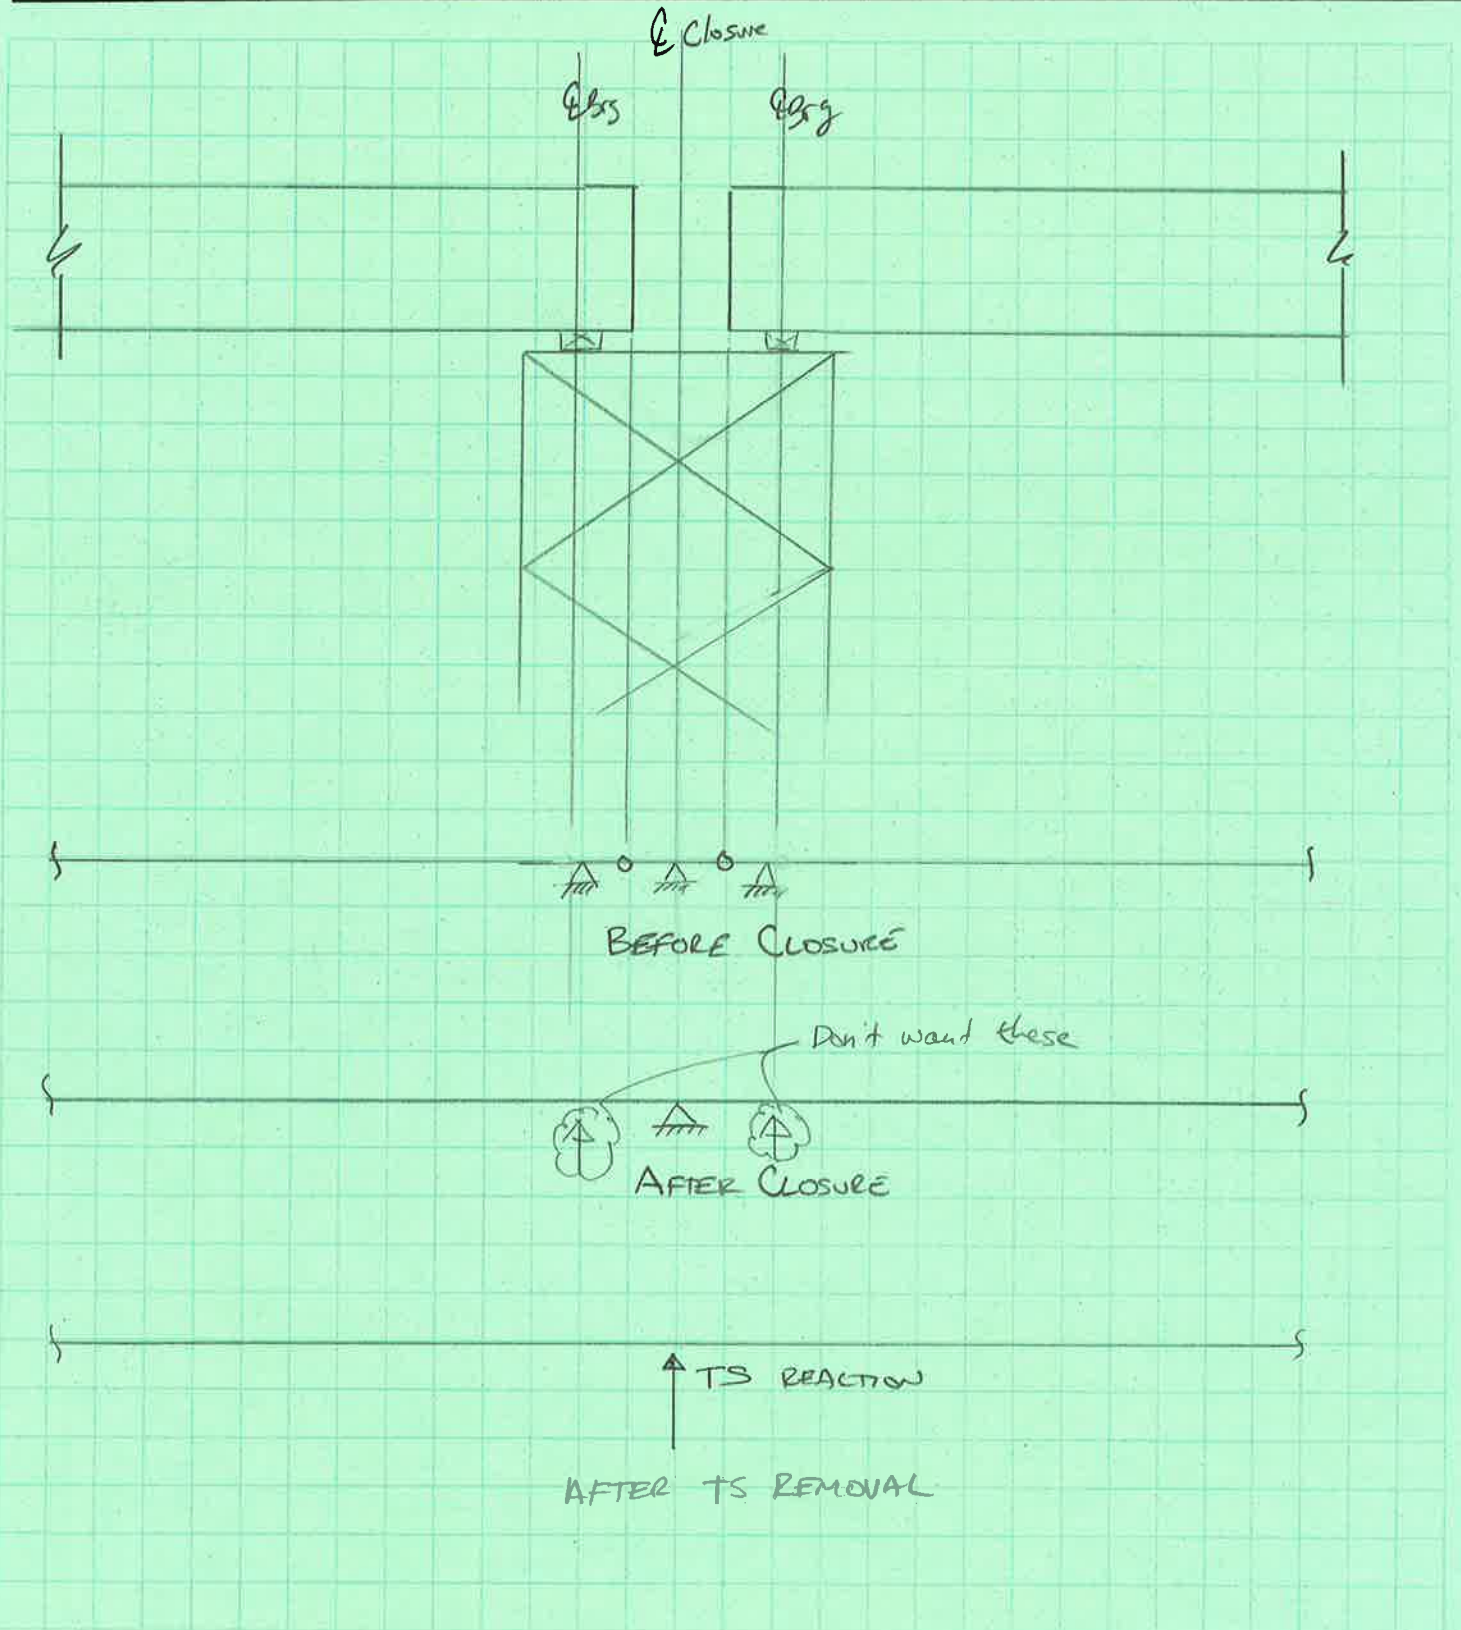




Project	LBAM @ STRONG BACK			
S.R.	Made By	Check by	Date	Sheet No. of
				Supv

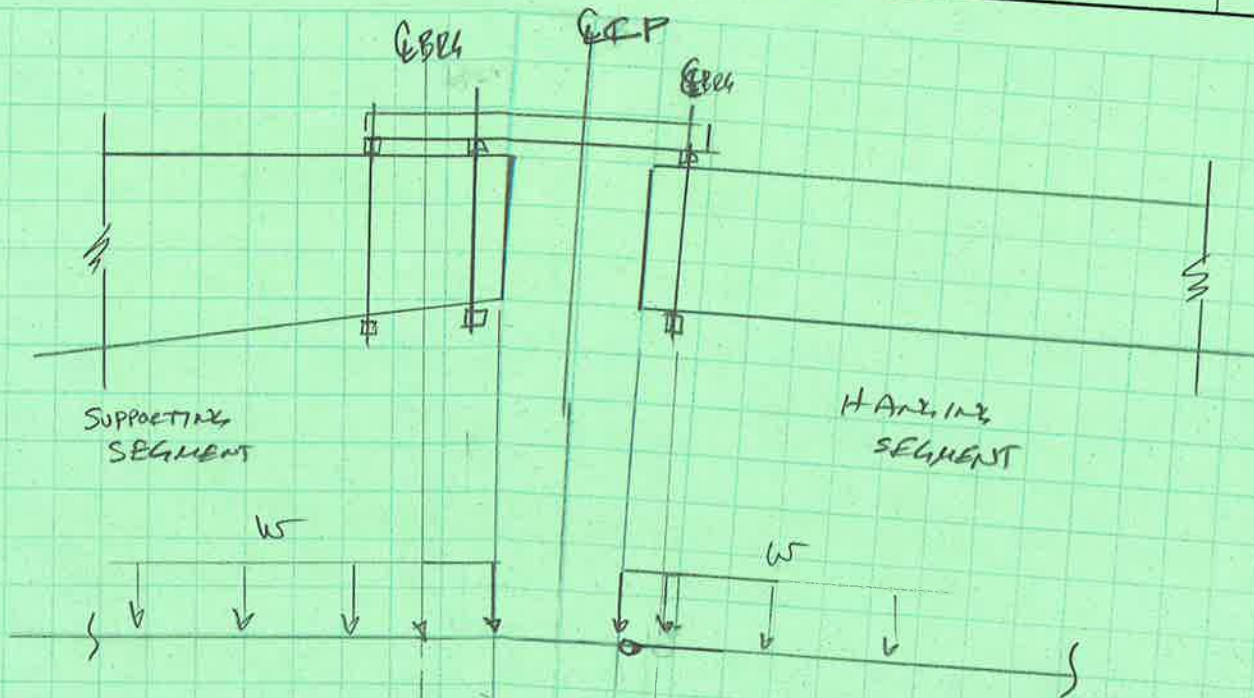




Bridge & Structures Design Calculations

Project				Sheet No.	of	Sheets
S.R.	Made By	Check by	Date	Supv		

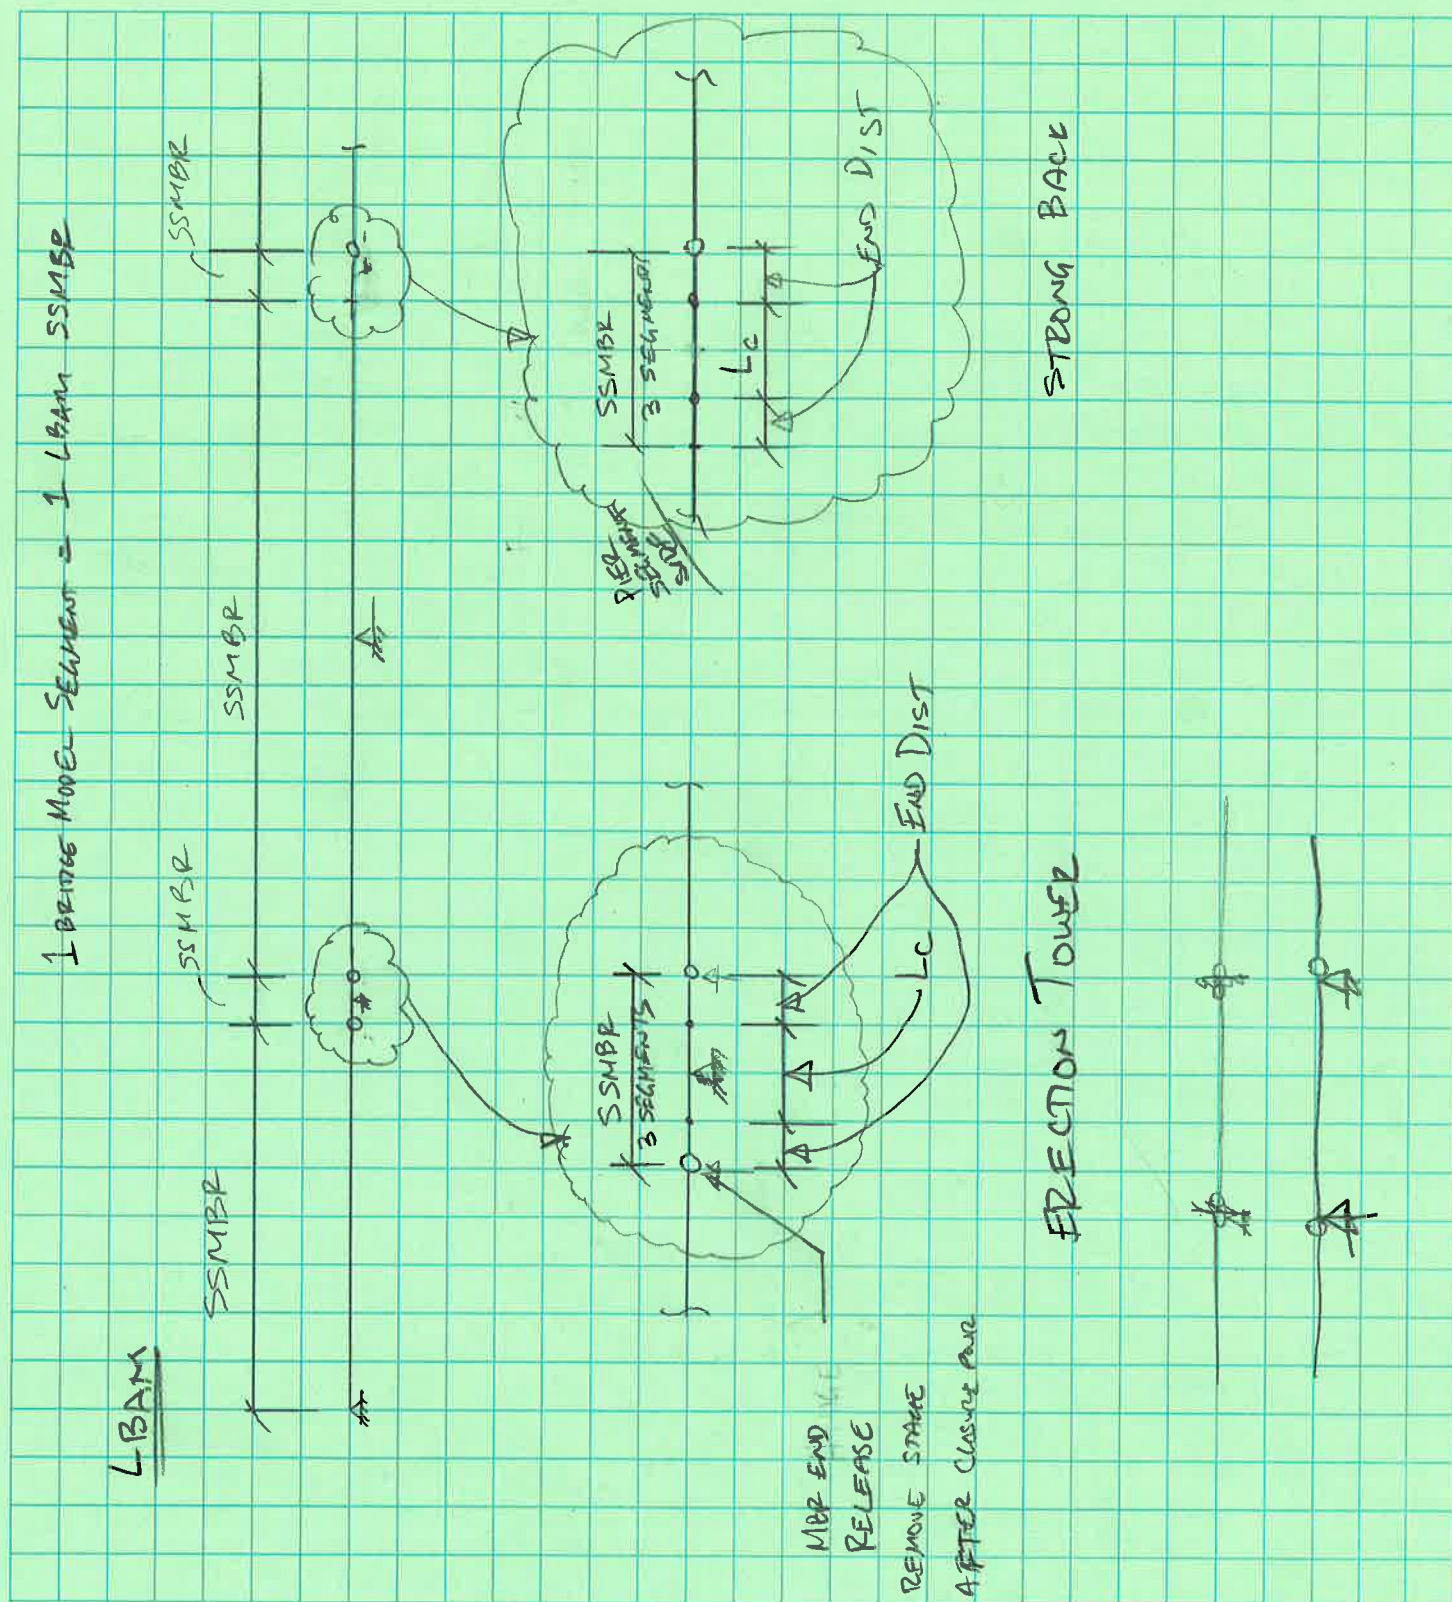




Project			Sheet No.	of	Sheets
S.R.	Made By	Check by	Date	Supv	

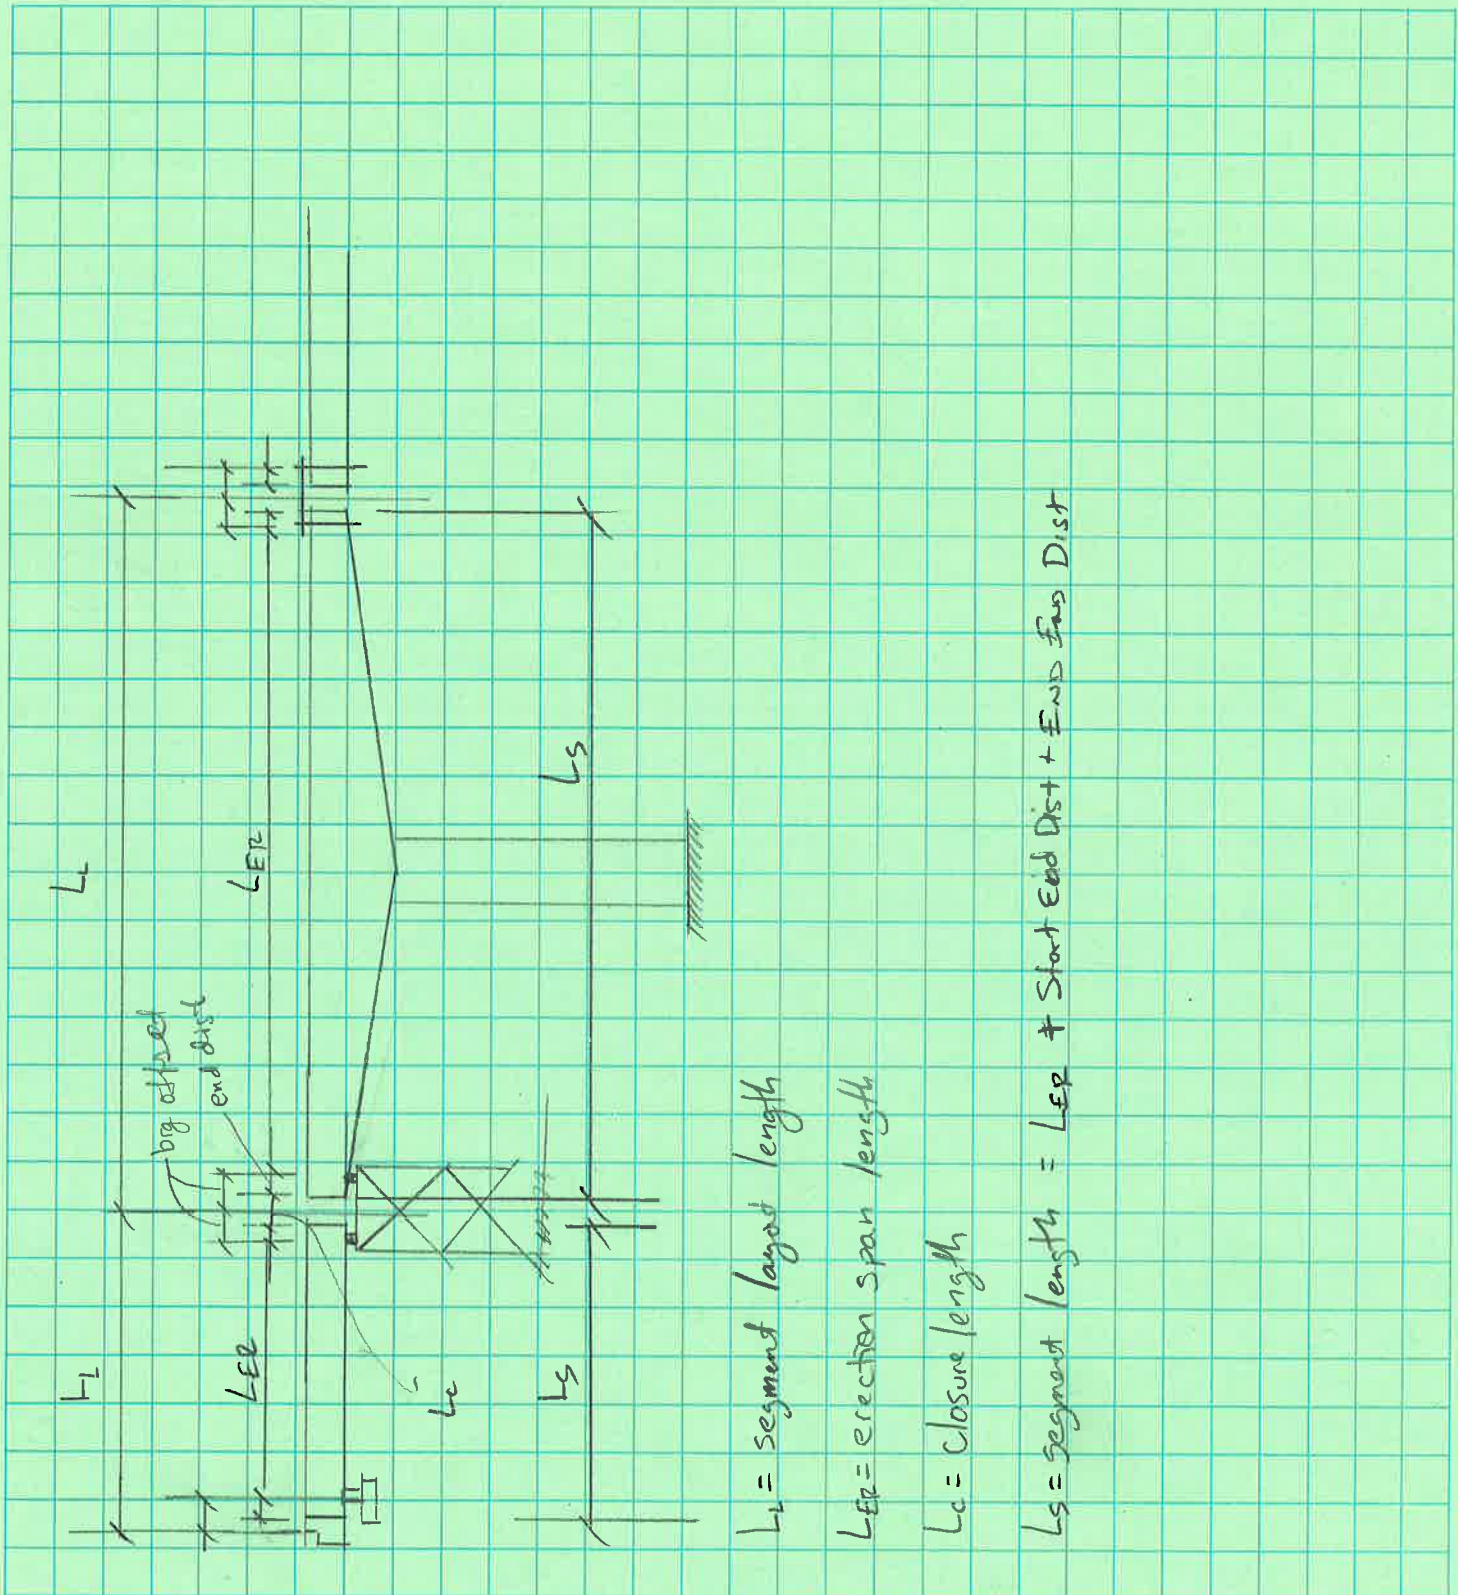



Project LBAM @ CONTINUITY PIER		Sheet No. of Sheets	
S.R.	Made By	Check by	Date
			Supv

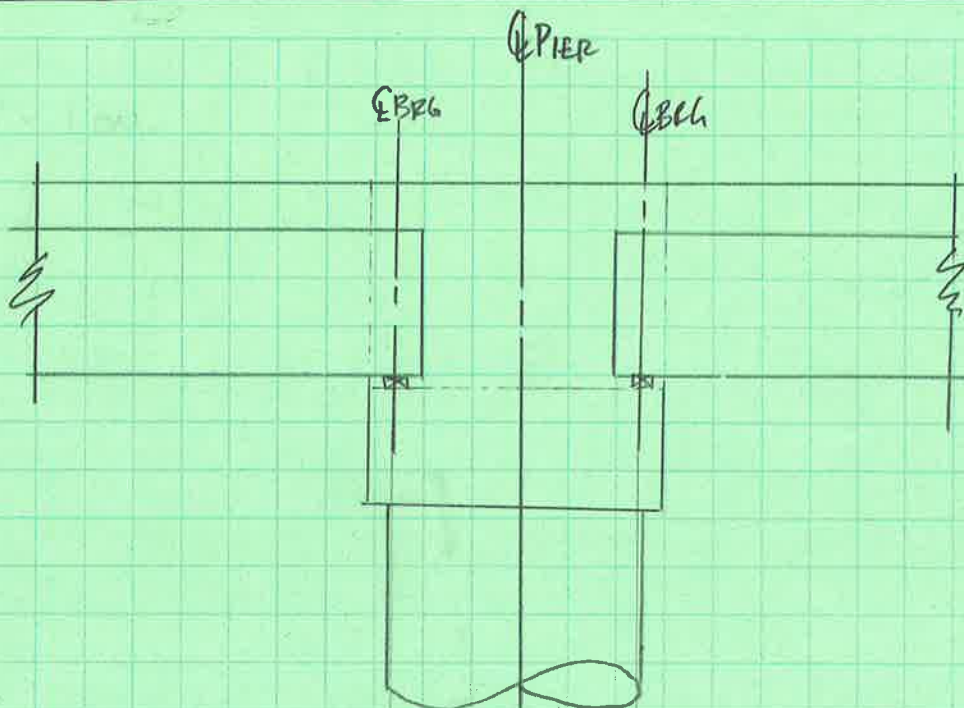


BEFORE CONTINUITY



AFTER CONTINUITY




Project			Sheet No. of Sheets	
S.R.	Made By	Check by	Date	Supv

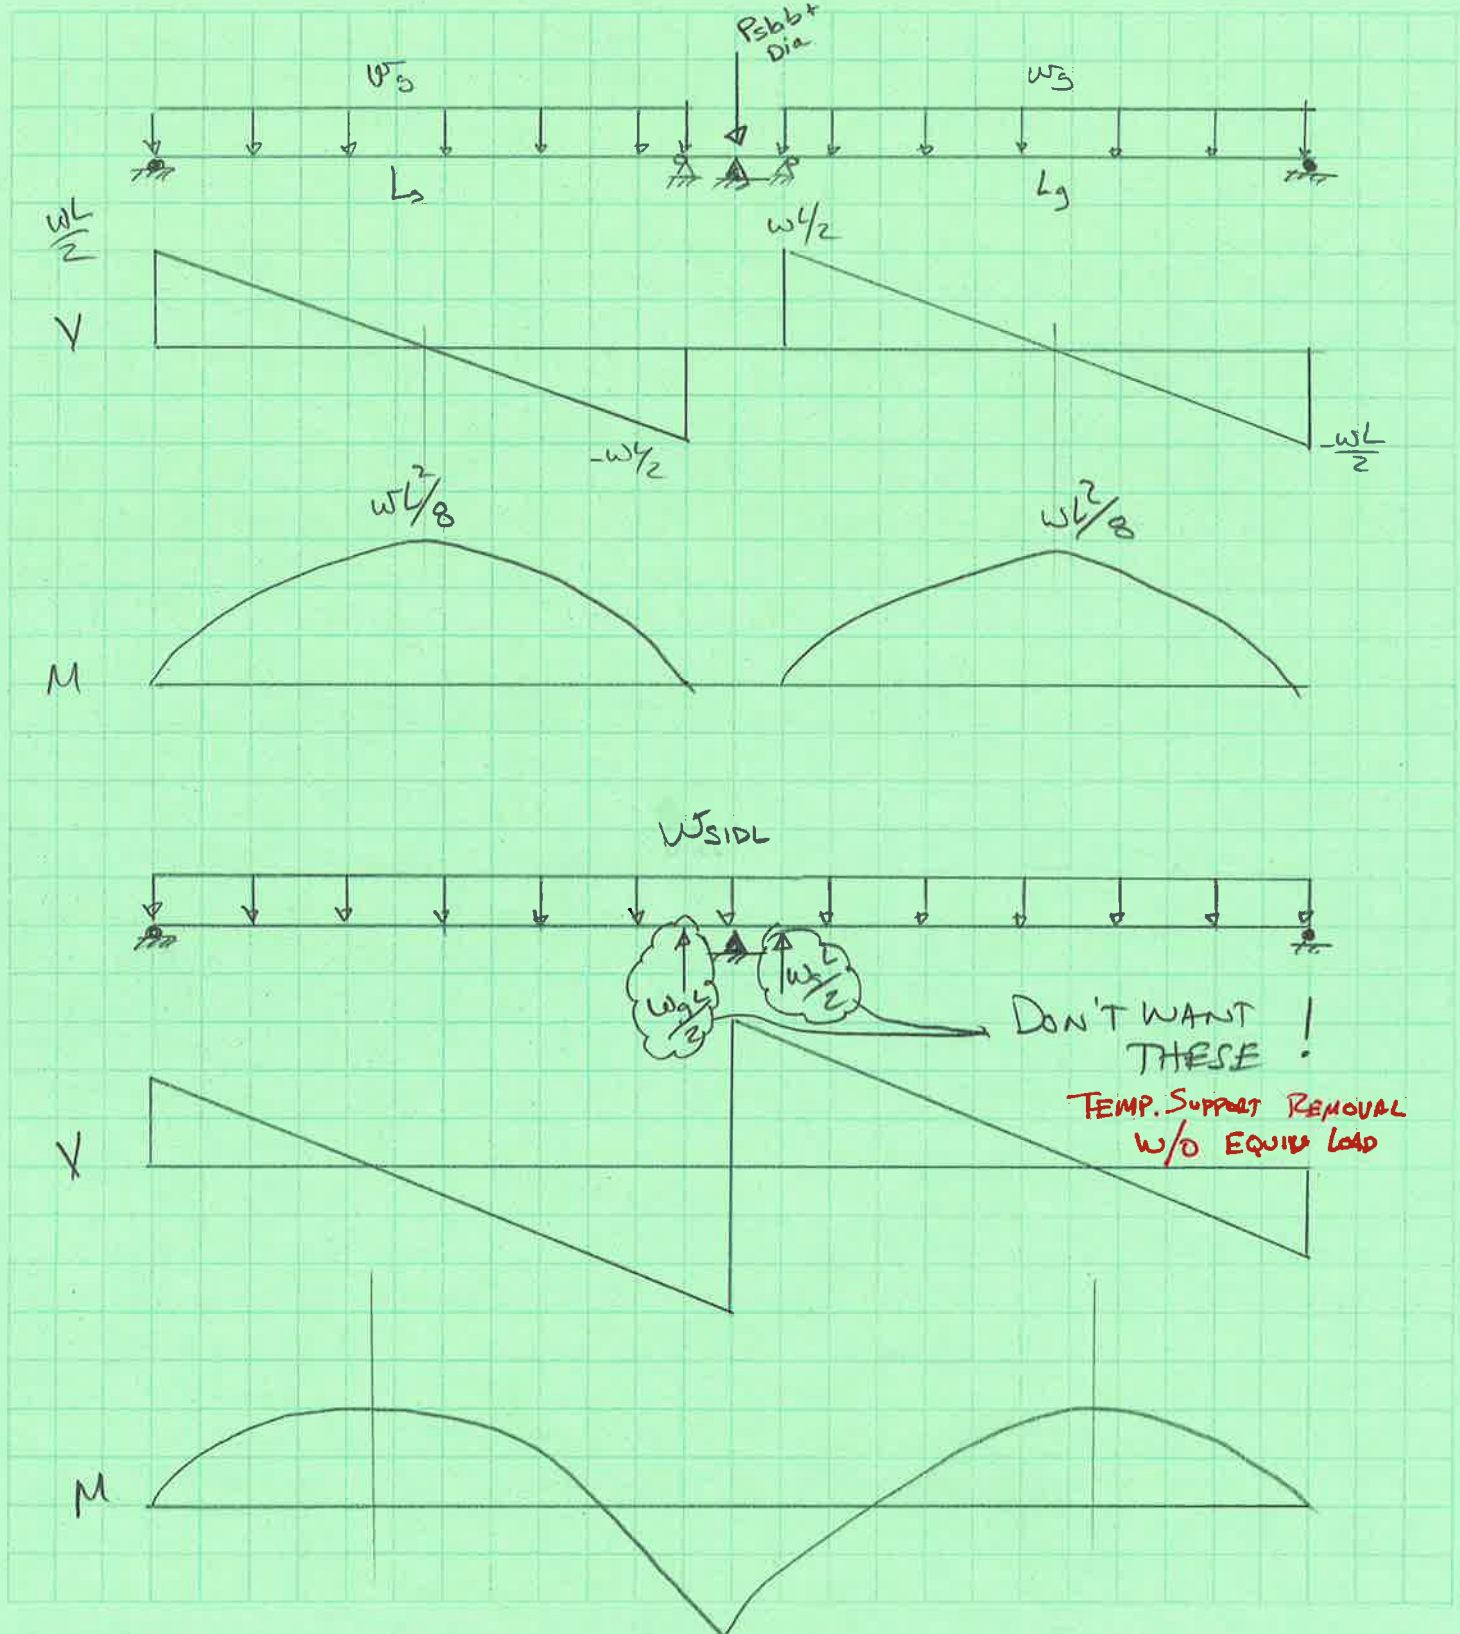



Project LBAM @ HINGE PIER		Sheet No. of Sheets	
S.R.	Made By	Check by	Date
			Supv

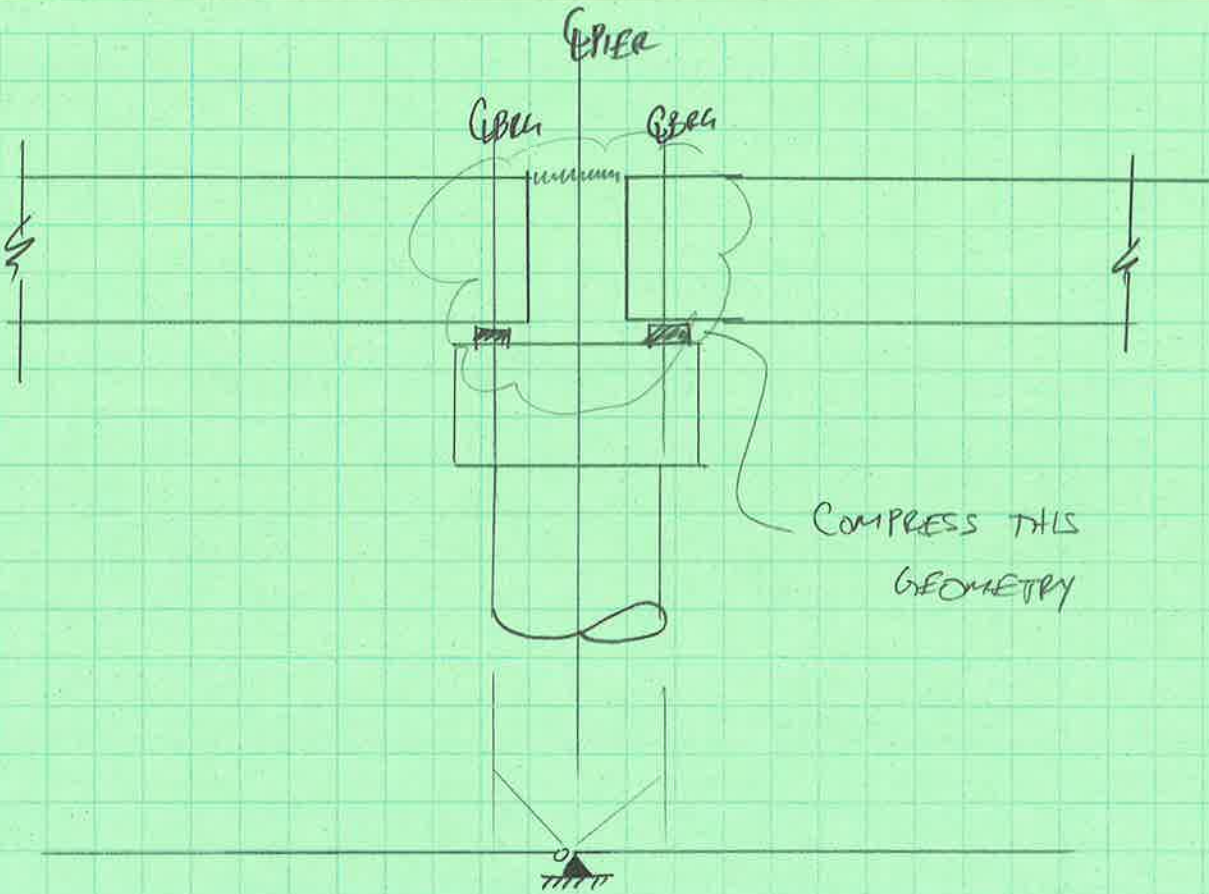



Project	LBAM @ ABUTMENT			Sheet No.	of	Sheets
S.R.	Made By	Check by	Date	Supv		

